
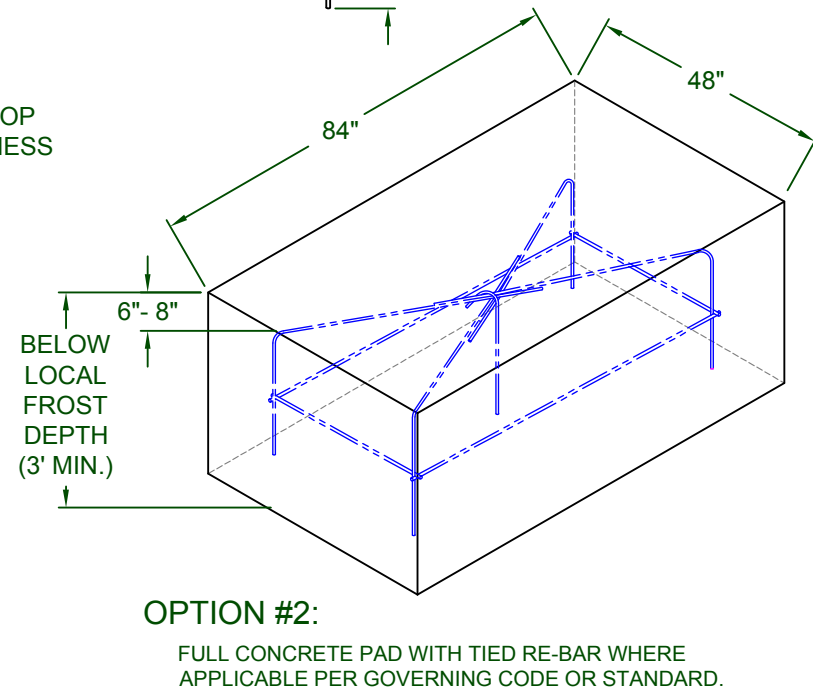
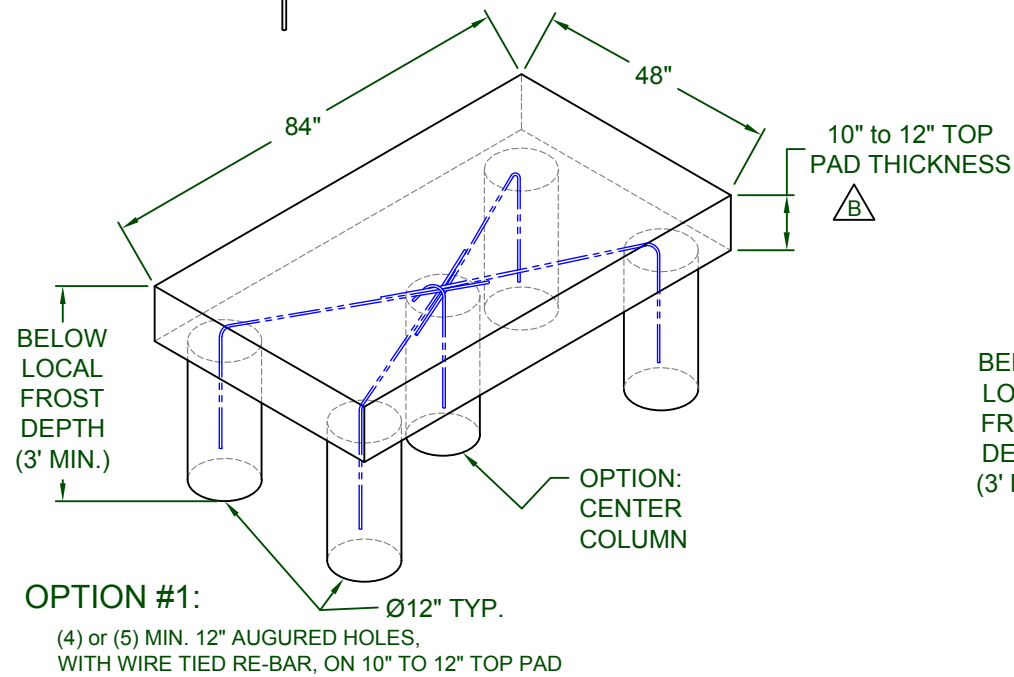
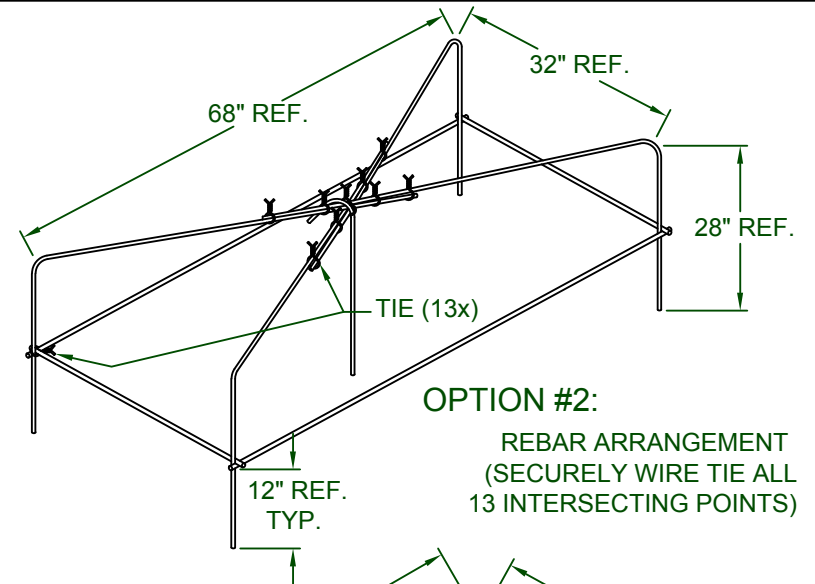


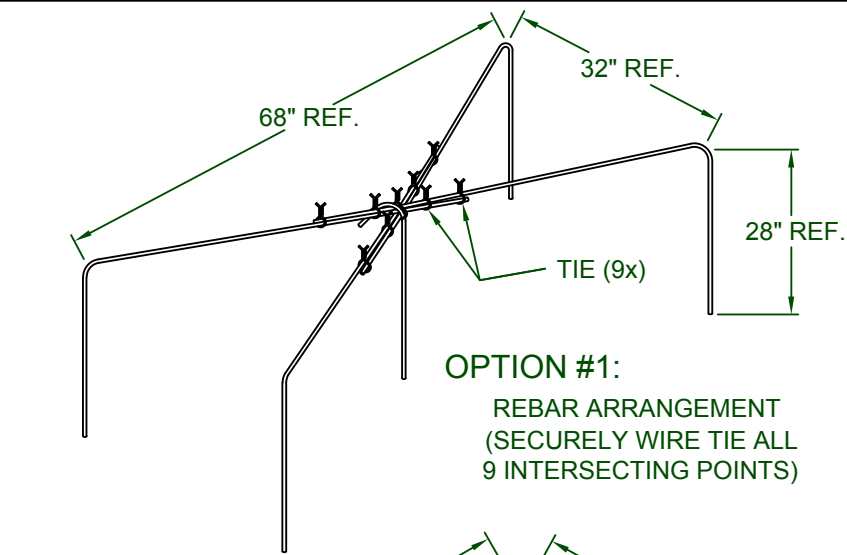

NOTES:

- 1) ALL PAD DEPTHS SHOULD BE BELOW LOCAL FROST DEPTH
- 2) TOP OF PAD MUST BE FLAT AND LEVEL
- 3) USE REBAR THAT CONFORMS WITH LOCAL CODES OR JOB SPECS.
- 4) REBAR MUST BE INSTALLED 6"-8" BELOW TOP SURFACE.
- 5) CONCRETE COMPRESSIVE STRENGTH MINIMUM 3000 PSI.
- 5) DRAWING IS FOR REFERENCE ONLY, SUPERCEDED BY LOCAL AND SITE GOVERNING CODES

DO NOT SCALE


Rev.:	Description:	Date:	Drn. By:	Ckd. By:
C	ENHANCED REBAR DETAIL	11/5/15	KAY	DMR
B	10" TO 12" PAD THICKNESS WAS 8" TO 10"	01/24/13	SLD	KLL
A	CONDUIT LOCATIONS WERE MOVED OUTSIDE THE PAD	07/18/08	MKS	DMR

NOTICE
THE INFORMATION CONTAINED ON THIS DOCUMENT IS CONFIDENTIAL. ANY DISSEMINATION, UNAPPROVED DISCLOSURE OR COPYING OF THIS INFORMATION IS STRICTLY PROHIBITED.
UNLESS OTHERWISE SPECIFIED DIMENSIONS ARE IN INCHES ANGLES $\pm 1^\circ$
X/X $\pm 1/32$, .XX $\pm .01$, .XXX $\pm .005$

Date:	12/21/05
Drn. By:	MKS
Ckd. By:	DMR
Dwg.:	102-P
Title:	Operator PAD Layout / Options



LEFTHAND OPERATOR

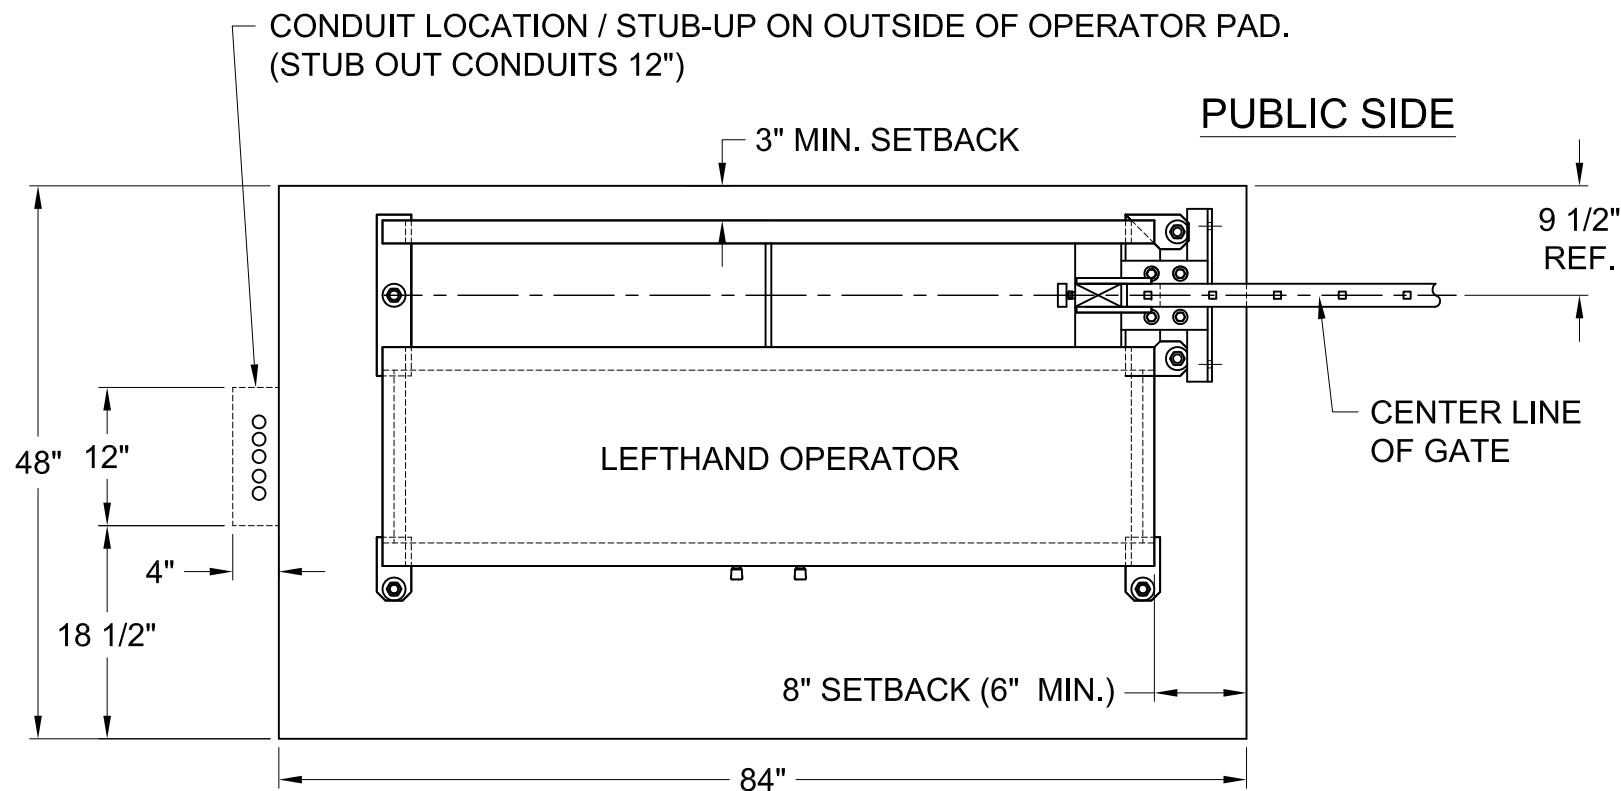

* NOTE: USE 3/4" CONDUIT ONLY


PRIVATE/SECURED SIDE

POSSIBLE CONDUITS

- * 120 VAC, MIN. 15 AMP CIRCUIT
- * "ENTRANCE" KEYPAD
- * "EXIT" KEYPAD
- * REVERSING/SAFETY LOOPS
- * FREE EXIT LOOP
- * OFFICE COMMUNICATION
- * IFR BEAM POWER
- * OPTIONAL SPARES

					NOTICE		Date: 12/07/05	 AutoGate Gate Entry Systems Berlin Heights, Ohio FAX (419) 588-3514
					THE INFORMATION CONTAINED ON THIS DOCUMENT IS CONFIDENTIAL. ANY DISSEMINATION, UNAPPROVED DISCLOSURE OR COPYING OF THIS INFORMATION IS STRICTLY PROHIBITED		Dwn. By: MKS	
							Ckd. By: DMR	
Rev.:	Description:	Date:	Dwn. By:	Ckd. By:	UNLESS OTHERWISE SPECIFIED DIMENSIONS ARE IN INCHES ANGLES ± 1° X/X ± 1/32, XX ± .01, XXX ± .005		Dwg.: 102C-L	Title: Conduit Pad Location (Lefthand)
C	LEFTHAND OPERATOR WAS VPL OPERATOR	04/29/15	MKS	KAY				
B	UPDATED DRAWING	01/23/13	SLD	DMR				
A	CONDUIT LOCATIONS WERE MOVED OUTSIDE THE PAD	07/18/08	MKS	DMR				

RIGHTHAND OPERATOR

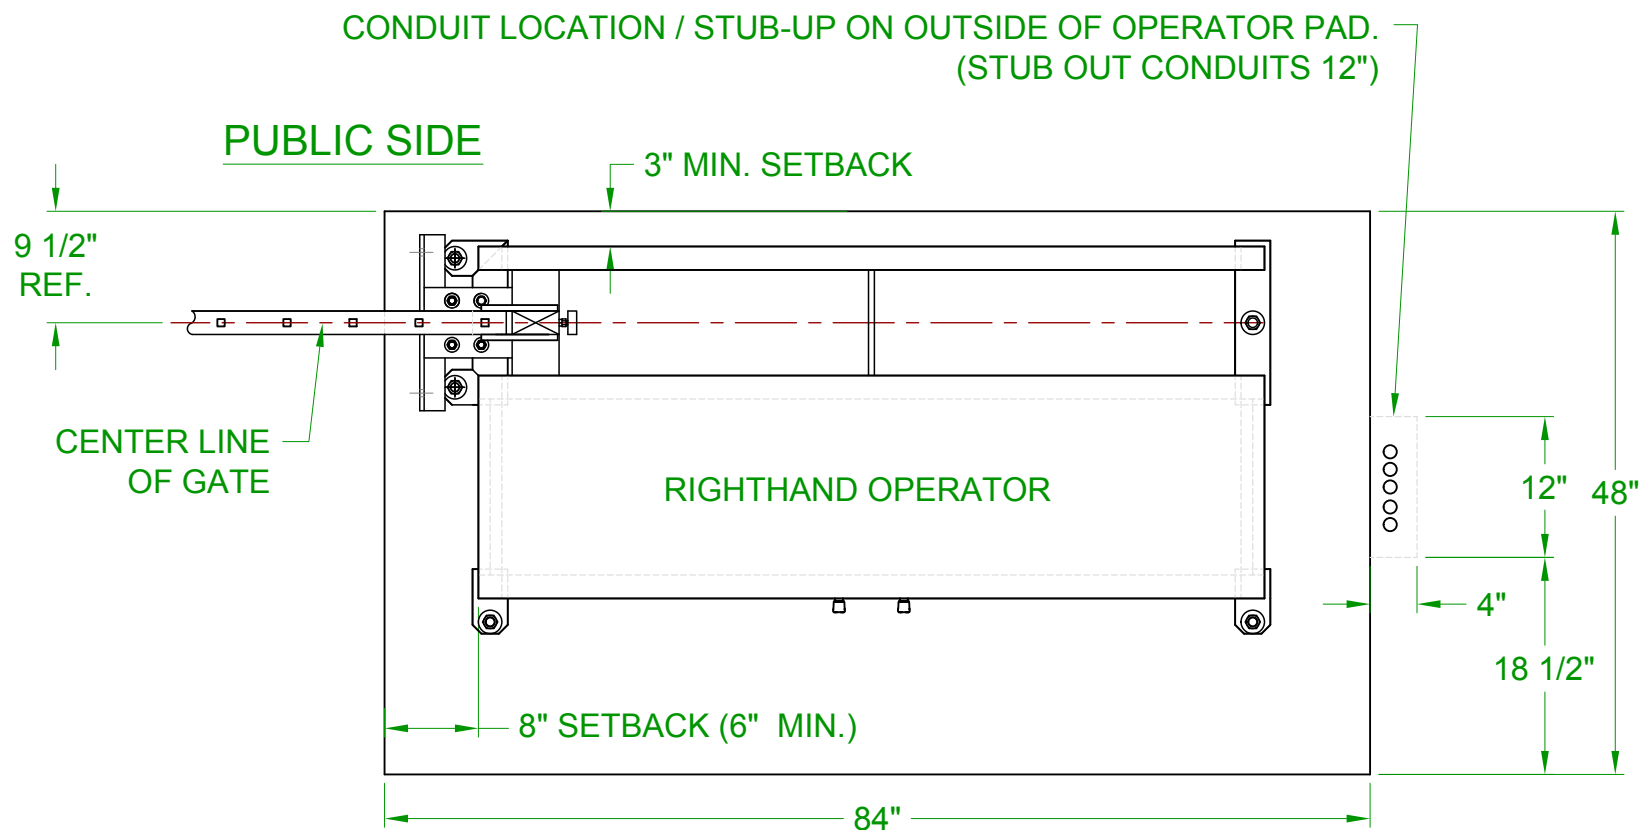

PRIVATE/SECURED SIDE

* NOTE: TYP 3/4" CONDUIT

POSSIBLE CONDUITS

- * 120 VAC, MIN. 15 AMP CIRCUIT
- * "ENTRANCE" KEYPAD
- * "EXIT" KEYPAD
- * REVERSING/SAFETY LOOPS
- * FREE EXIT LOOP
- * OFFICE COMMUNICATION
- * IFR BEAM POWER
- * OPTIONAL SPARES


DO NOT SCALE				
Rev.:	Description:	Date:	Drn. By:	Ckd. By:
C	RIGHTHAND OPERATOR WAS VPL OPERATOR	04/29/15	MKS	KAY
B	UPDATED PRINT	1/24/13	SLD	DMR
A	CONDUIT LOCATIONS WERE MOVED OUTSIDE THE PAD	07/18/08	MKS	DMR

NOTICE	
THE INFORMATION CONTAINED ON THIS DOCUMENT IS CONFIDENTIAL. ANY DISSEMINATION, UNAPPROVED DISCLOSURE OR COPYING OF THIS INFORMATION IS STRICTLY PROHIBITED.	
UNLESS OTHERWISE SPECIFIED DIMENSIONS ARE IN INCHES ANGLES ± 1° X/X ± 1/32, .XX ± .01, .XXX ± .005	

Date:	12/07/05
Drn. By:	MKS
Ckd. By:	DMR
Dwg.:	102C-R
Title:	Conduit Pad Location (Righthand)

	AutoGate
	Gate Entry Systems
Berlin Heights, Ohio FAX (419) 588-3514	

LEFTHAND OPERATOR

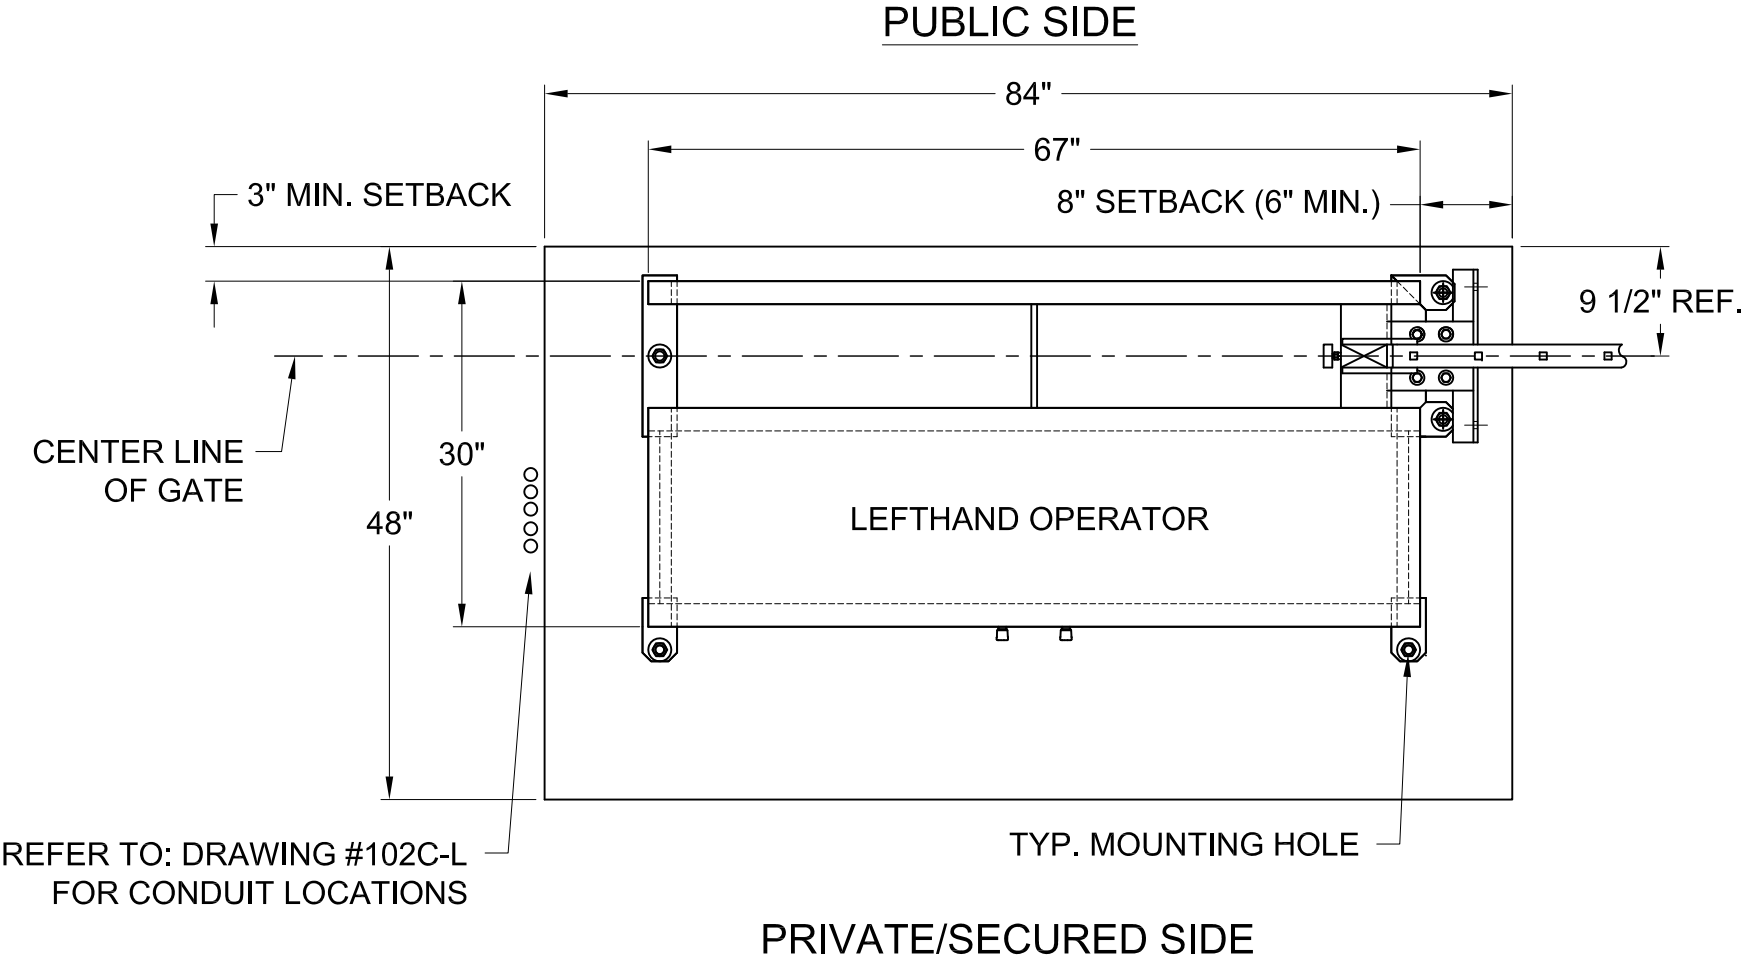


REFER TO: DRAWING #102C-L
FOR CONDUIT LOCATIONS

NOTES:

- 1) PAD DIMENSIONS CAN VARY PER SITE
- 2) LEAVE AT LEAST 3" BETWEEN ANCHOR AND EDGE OF PAD
- 3) ALL PADS MUST BE POURED LEVEL AND BELOW LOCAL FROST LINE DEPTH

					DO NOT SCALE		NOTICE		Date: 12/07/05	 AutoGate Gate Entry Systems Berlin Heights, Ohio FAX (419) 588-3514
Rev.:	Description:			Date:	Drn. By:	Ckd. By:	THE INFORMATION CONTAINED ON THIS DOCUMENT IS CONFIDENTIAL. ANY DISSEMINATION, UNAPPROVED DISCLOSURE OR COPYING OF THIS INFORMATION IS STRICTLY PROHIBITED.	Drn. By: MKS		
D	LEFTHAND OPERATOR WAS VPL OPERATOR			04/29/15	MKS	KAY		Ckd. By: DMR		
C	UPDATED PRINT			1/23/13	SLD	DMR				
B	REMOVED "STUB CONDUITS UNDER OPERATOR WHEN POSSIBLE" NOTE			02/04/10	MKS	DMR	UNLESS OTHERWISE SPECIFIED DIMENSIONS ARE IN INCHES ANGLES ± 1° X/X ± 1/32, .XX ± .01, .XXX ± .005	Dwg.: 102-L		
A	CONDUIT LOCATIONS WERE MOVED OUTSIDE THE PAD			07/18/08	MKS	DMR		Title: Standard Pad Layout (Left hand)		

RIGHTHAND OPERATOR

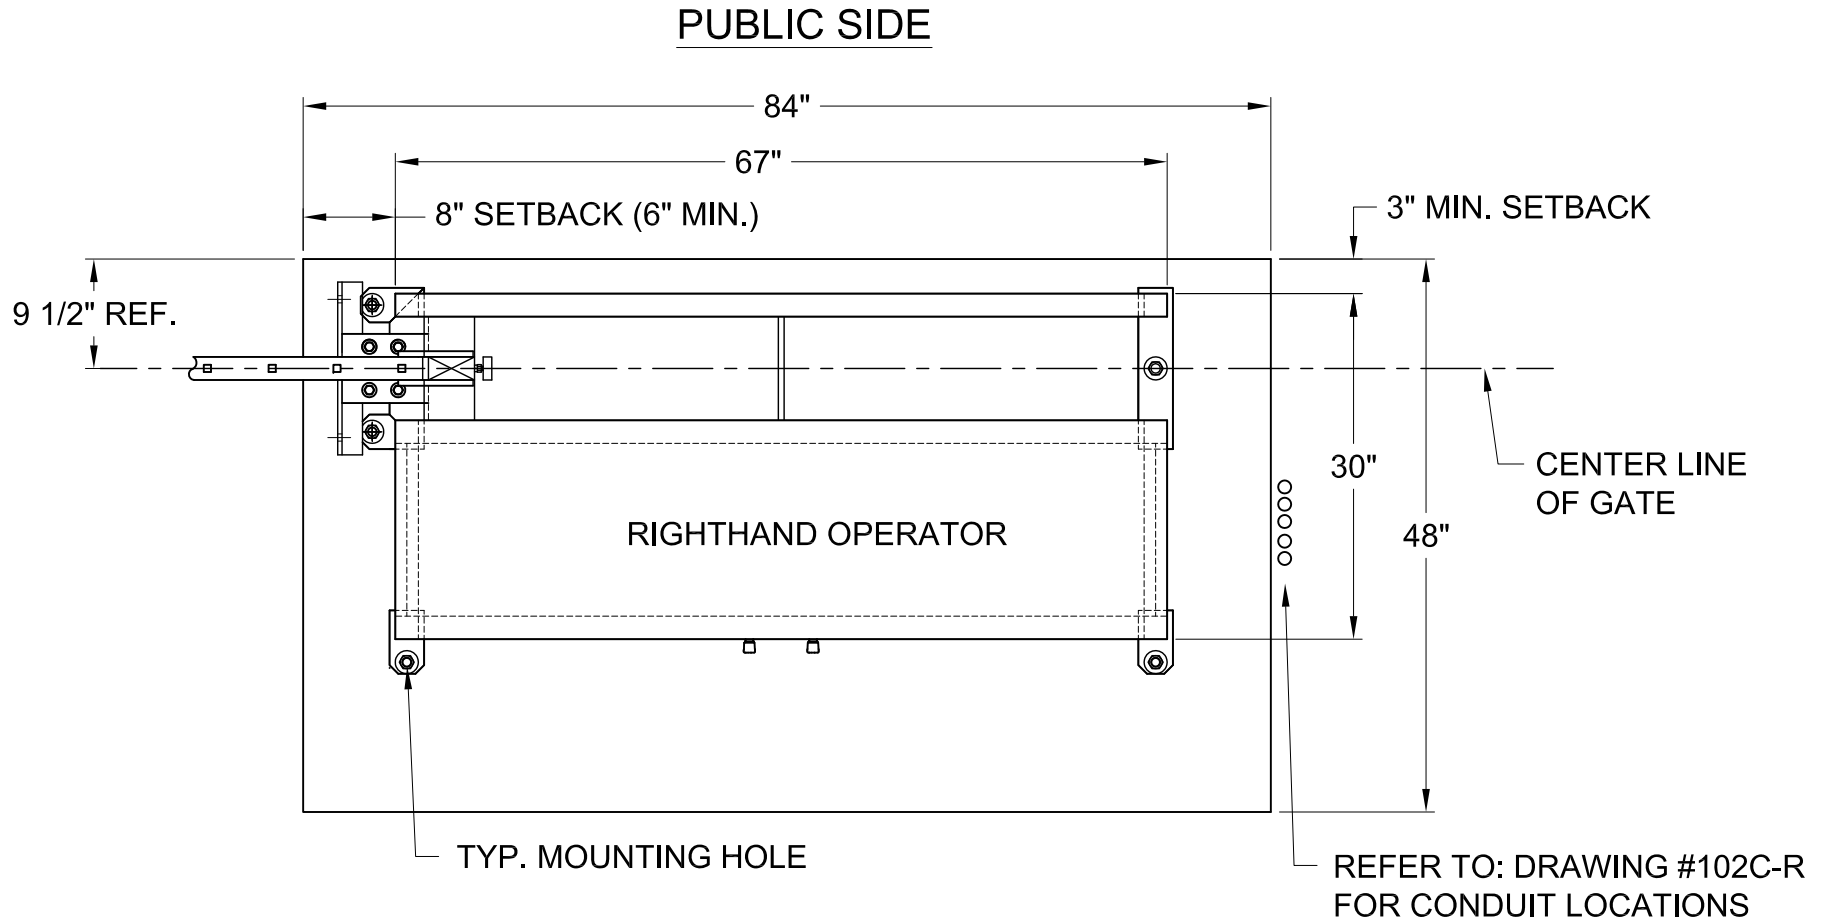

PRIVATE/SECURED SIDE

NOTES:

- 1) PAD DIMENSIONS CAN VARY PER SITE
- 2) LEAVE AT LEAST 3" BETWEEN ANCHOR AND EDGE OF PAD
- 3) ALL PADS MUST BE POURED LEVEL AND BELOW LOCAL FROST LINE DEPTH

			DO NOT SCALE		NOTICE THE INFORMATION CONTAINED ON THIS DOCUMENT IS CONFIDENTIAL. ANY DISSEMINATION, UNAPPROVED DISCLOSURE OR COPYING OF THIS INFORMATION IS STRICTLY PROHIBITED. UNLESS OTHERWISE SPECIFIED DIMENSIONS ARE IN INCHES ANGLES ± 1° X/X ± 1/32, .XX ± .01, .XXX ± .005	Date: 12/07/05	 AutoGate Gate Entry Systems Berlin Heights, Ohio FAX (419) 588-3514
Rev.:	Description:	Date:	Drn. By:	Ckd. By:		Drn. By: MKS	
D	RIGHTHAND OPERATOR WAS VPL OPERATOR	04/29/15	MKS	KAY		Ckd. By: DMR	
C	UPDATED DRAWING	1/24/13	SLD	DMR		Dwg.: 102-R	Title: Standard Pad Layout (Righthand)
B	REMOVED "STUB CONDUITS UNDER OPERATOR WHEN POSSIBLE" NOTE	02/04/10	MKS	DMR			
A	CONDUIT LOCATIONS WERE MOVED OUTSIDE THE PAD	07/18/08	MKS	DMR			