


# 8' HYDRAULIC LEFT HAND OPERATOR

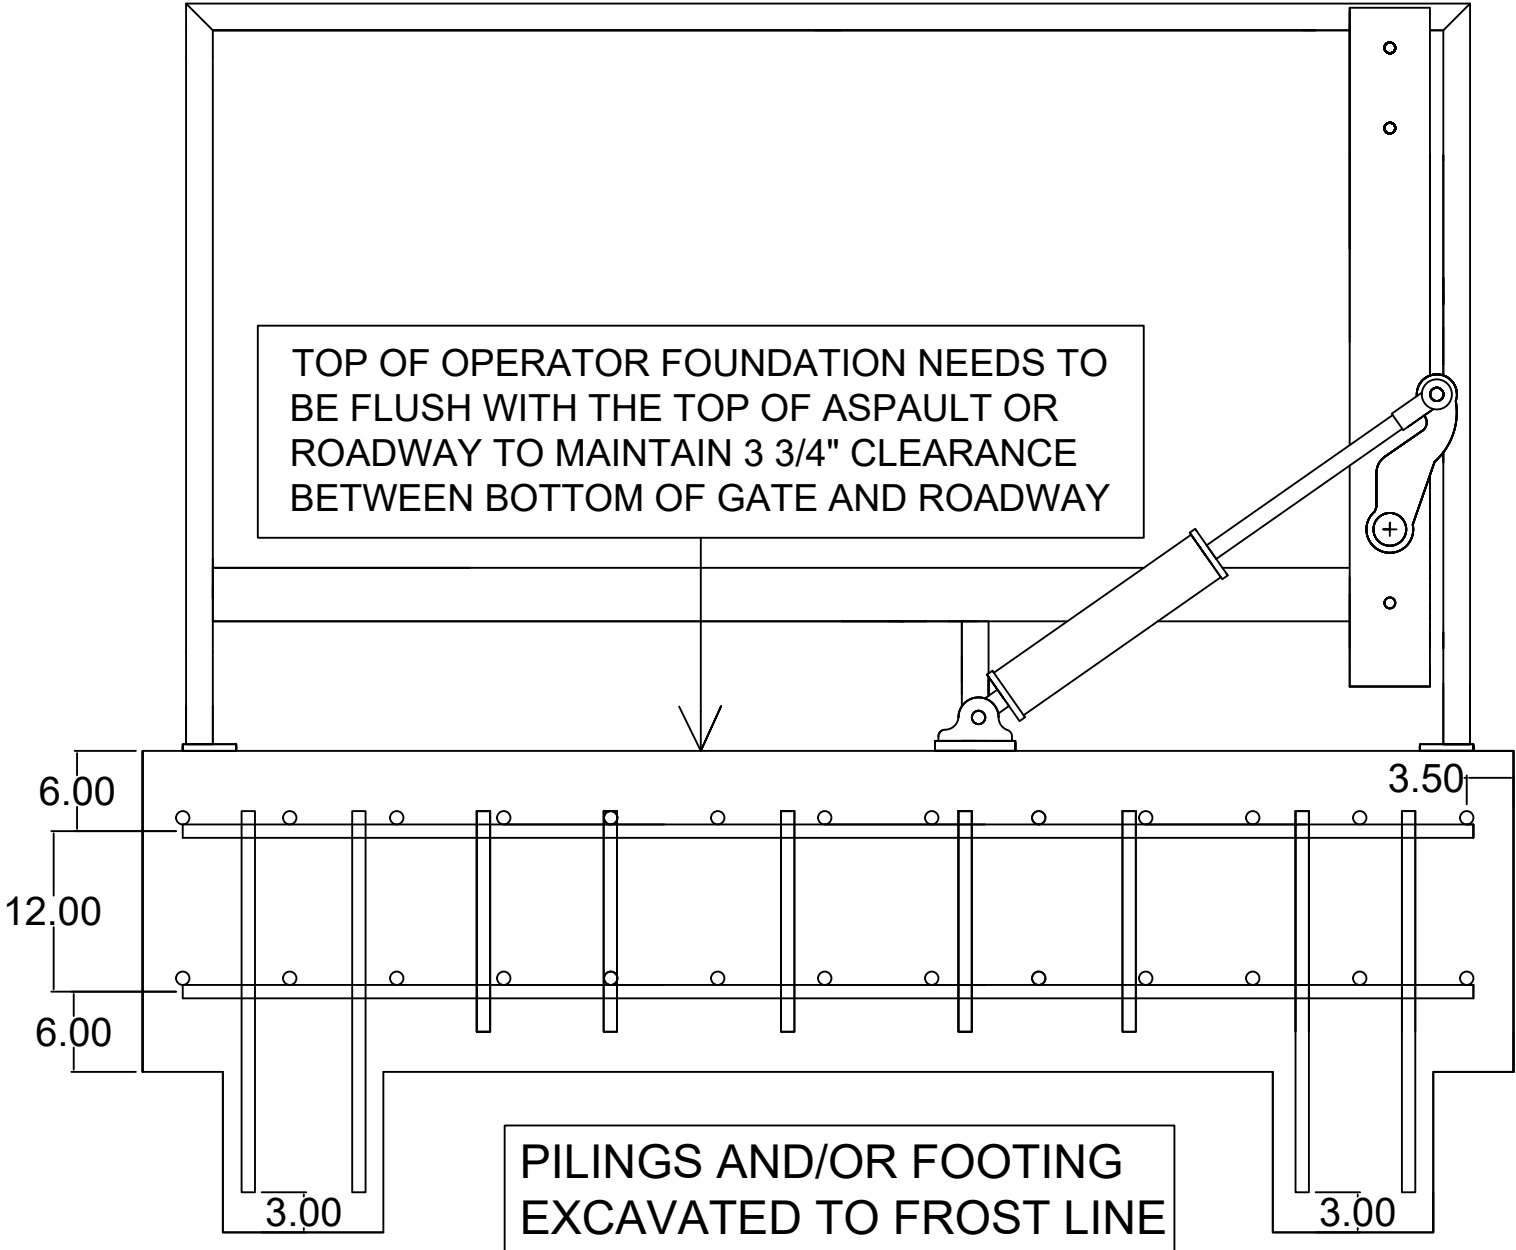

## CONCRETE NOTES:

THE COMPRESSIVE STRENGTH OF THE CONCRETE FOR FOUNDATION CONCRETE SHALL BE 3000 PSI, OR GREATER.

SITE TO BE WELL DRAINED, OVER EXCAVATE FOOTING 12" AND PLACE 1 INCH MINUS ANGULAR CRUSHED AGGREGATE UNDER FOOTING. COMPACT TO 95% RELATIVE DENSITY

SOIL BEARING ASSUMED TO BE 1500% PSI. IF UNSUITABLE SOIL IS ENCOUNTERED CONTACT ENGINEER OF RECORD.

#3 REBAR (VERTICAL) ON 16" CENTERS  
#4 REBAR MAT (HORIZONTAL) ON 8" CENTERS

\*EXTEND #3 REBAR TO 3" ABOVE FINAL DEPTH OF CONCRETE


## LEFT HAND OPERATOR 8' LEFT HAND OPERATOR



# 8' HYDRAULIC LEFT HAND OPERATOR

Secure Gate Operator to Concrete foundation using quantity 6 - Hilti KWIK BOLT TZ 304 Stainless wedge anchors (5/8" Diameter x 8.5" long)  
- Minimum effective embed depth = 4"

SECURE SIDE OF PROPERTY

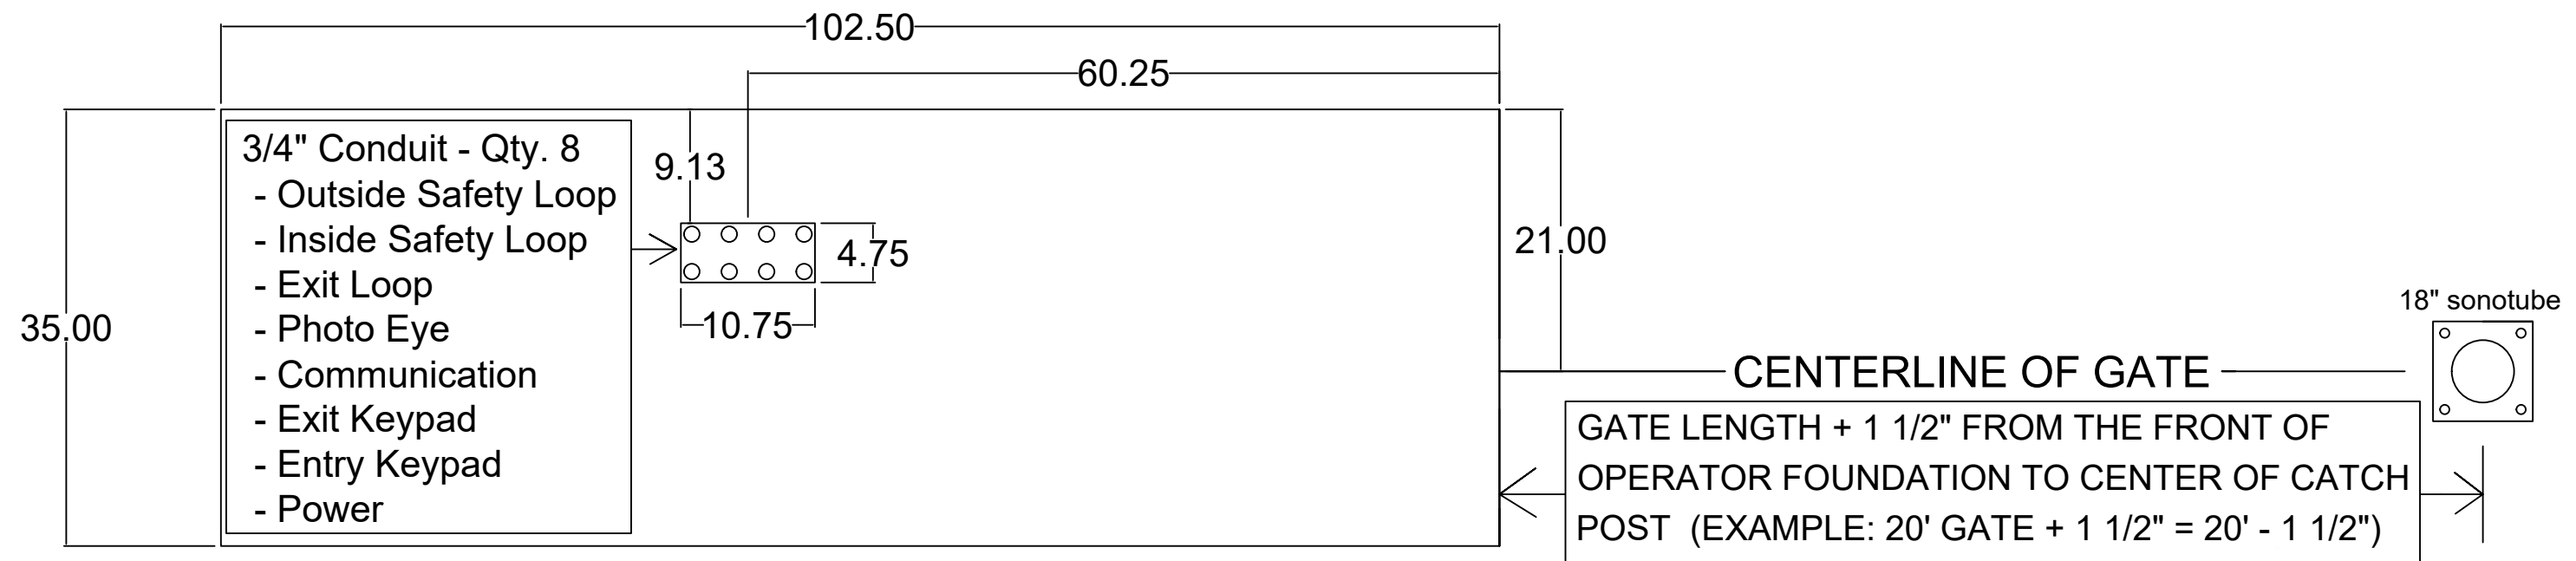


UNSECURE SIDE OF PROPERTY

8' LEFT HAND OPERATOR



# 8' HYDRAULIC LEFT HAND OPERATOR

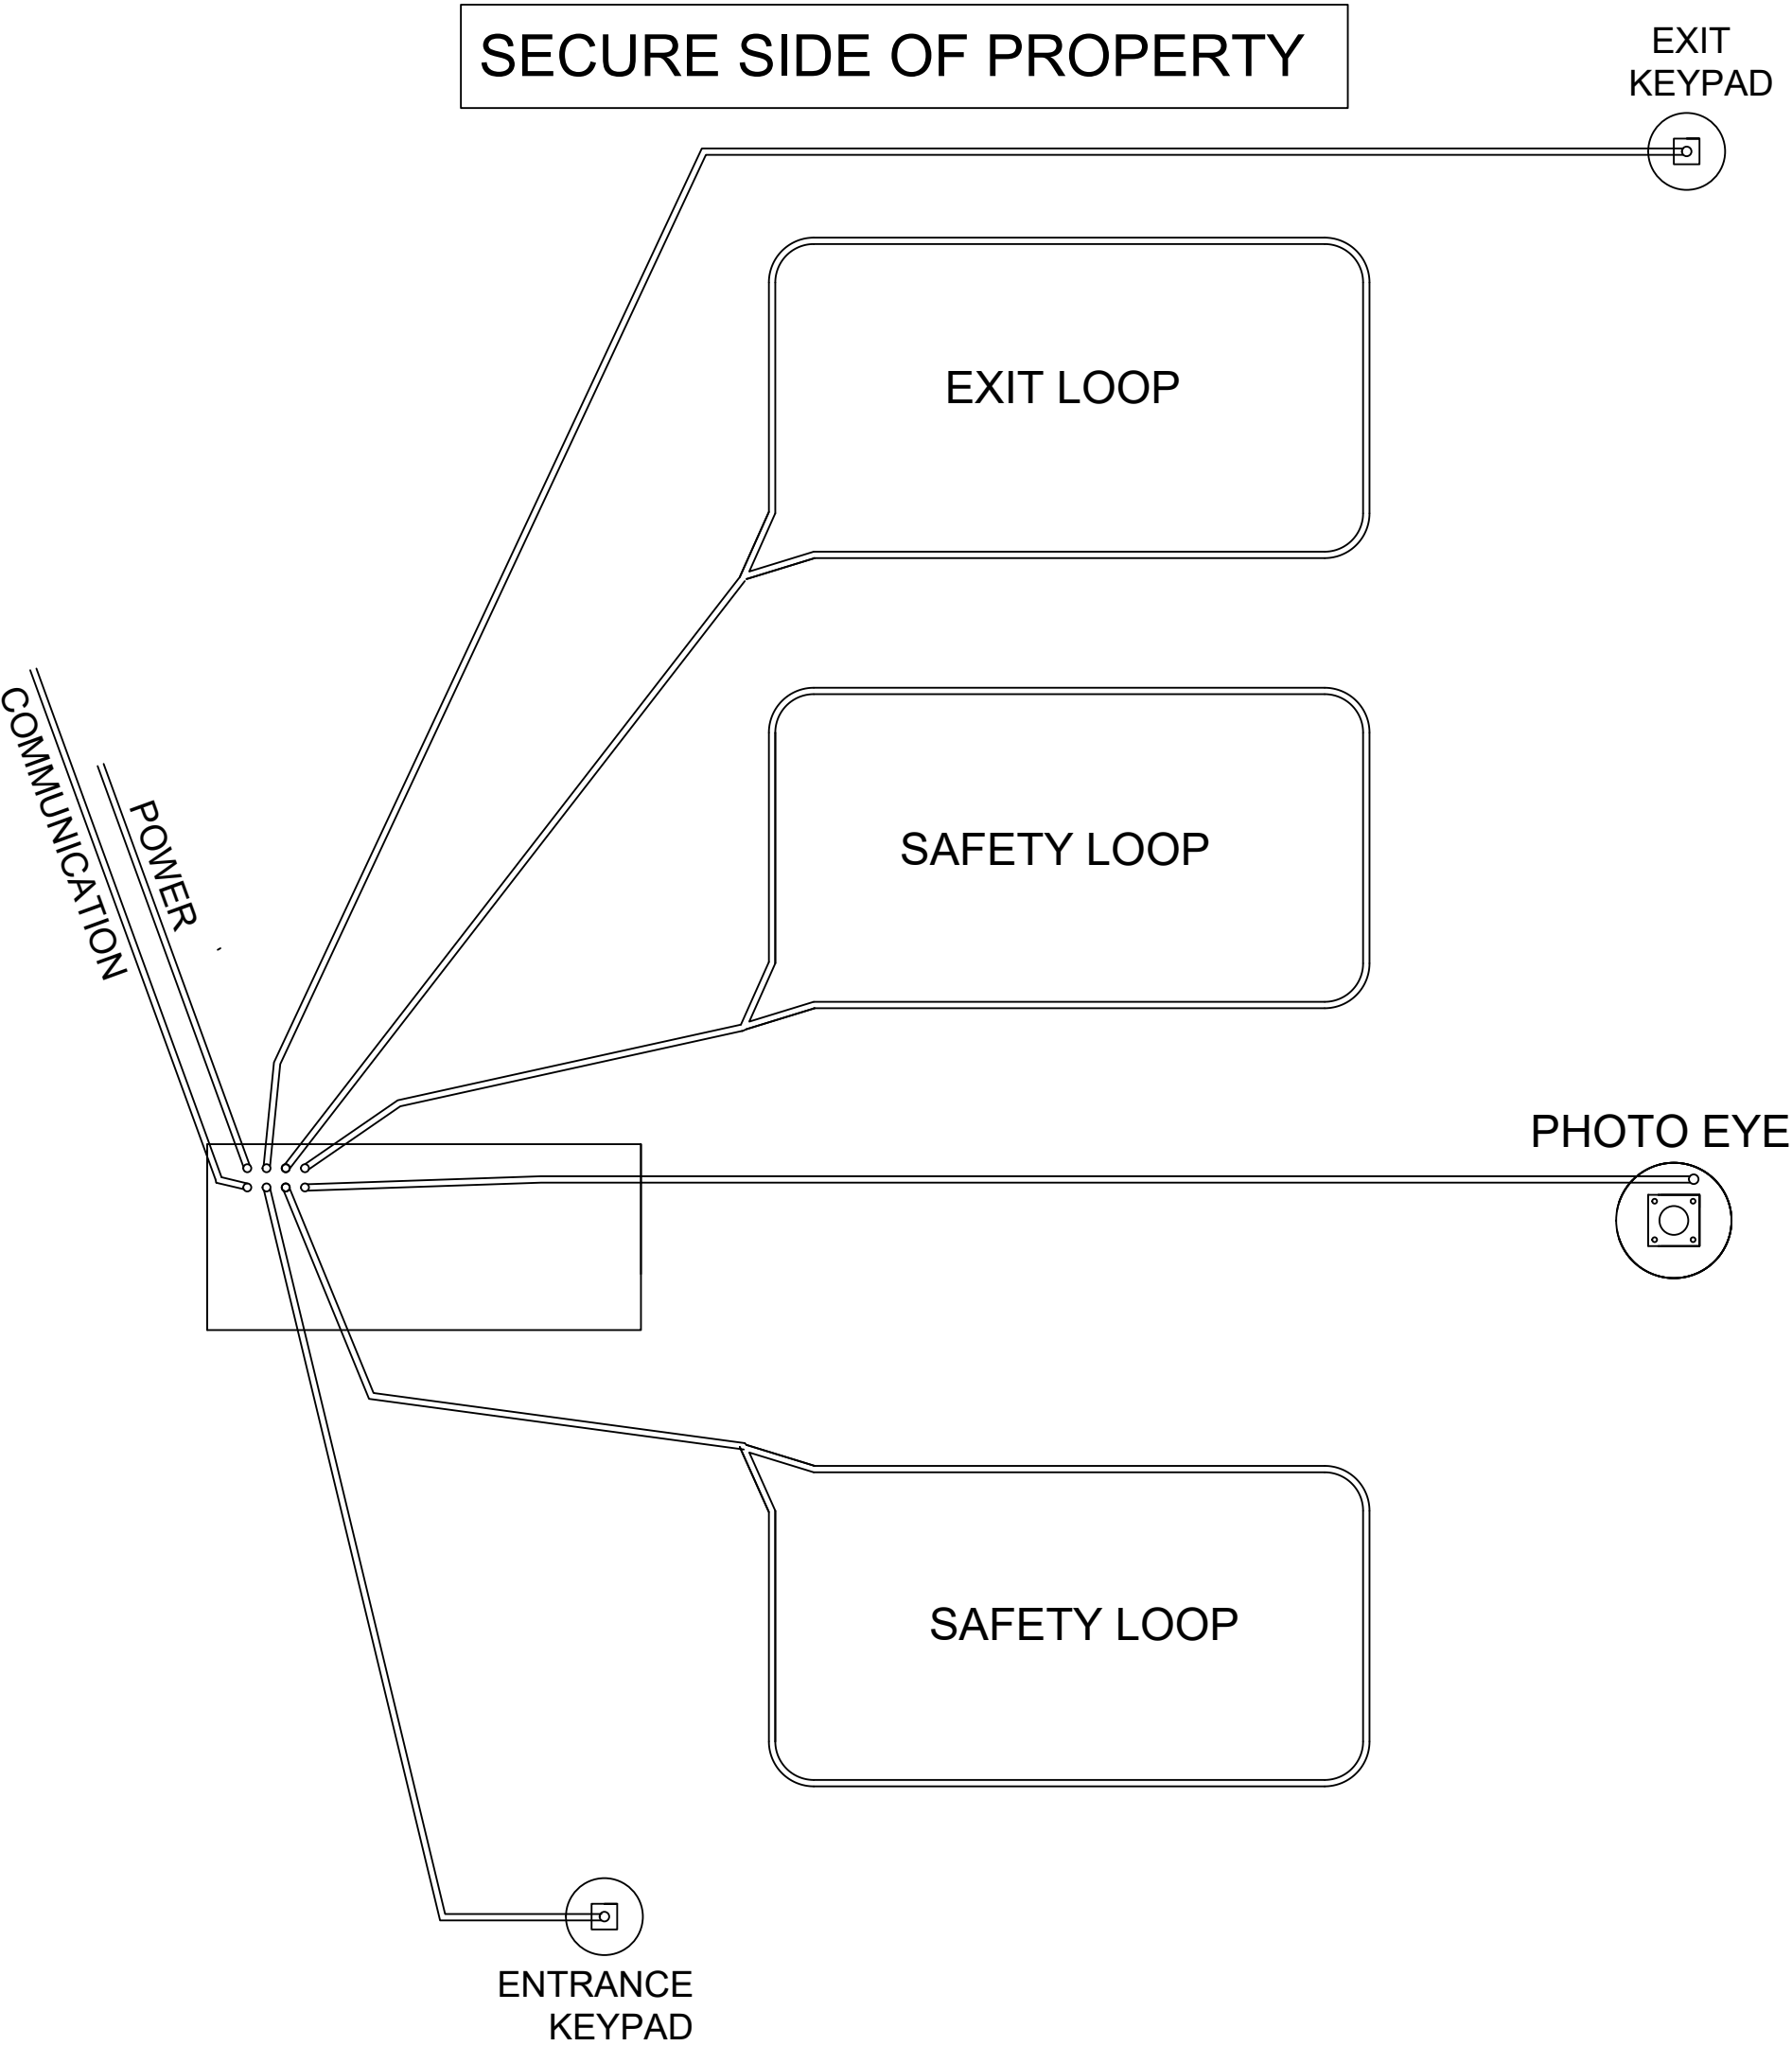

CONDUIT LAYOUT SHOWN FOR LEFT HAND OPERATOR  
\*DRAWING IS FOR REFERENCE ONLY

