

8' Hydraulic Right Hand Operator

CONCRETE NOTES:

THE COMPRESSIVE STRENGTH OF THE CONCRETE FOR FOUNDATION CONCRETE SHALL BE 3000 PSI, OR GREATER.

SITE TO BE WELL DRAINED, OVER EXCAVATE FOOTING 12" AND PLACE 1 INCH MINUS ANGULAR CRUSHED AGGREGATE UNDER FOOTING. COMPACT TO 95% RELATIVE DENSITY

SOIL BEARING ASSUMED TO BE 1500% PSI. IF UNSUITABLE SOIL IS ENCOUNTERED CONTACT ENGINEER OF RECORD.


#3 REBAR (VERTICAL) ON 16" CENTERS

#4 REBAR MAT (HORIZONTAL) ON 8" CENTERS

*EXTEND #3 REBAR TO 3" ABOVE FINAL DEPTH OF CONCRETE


RIGHT HAND OPERATOR

8' RIGHT HAND OPERATOR

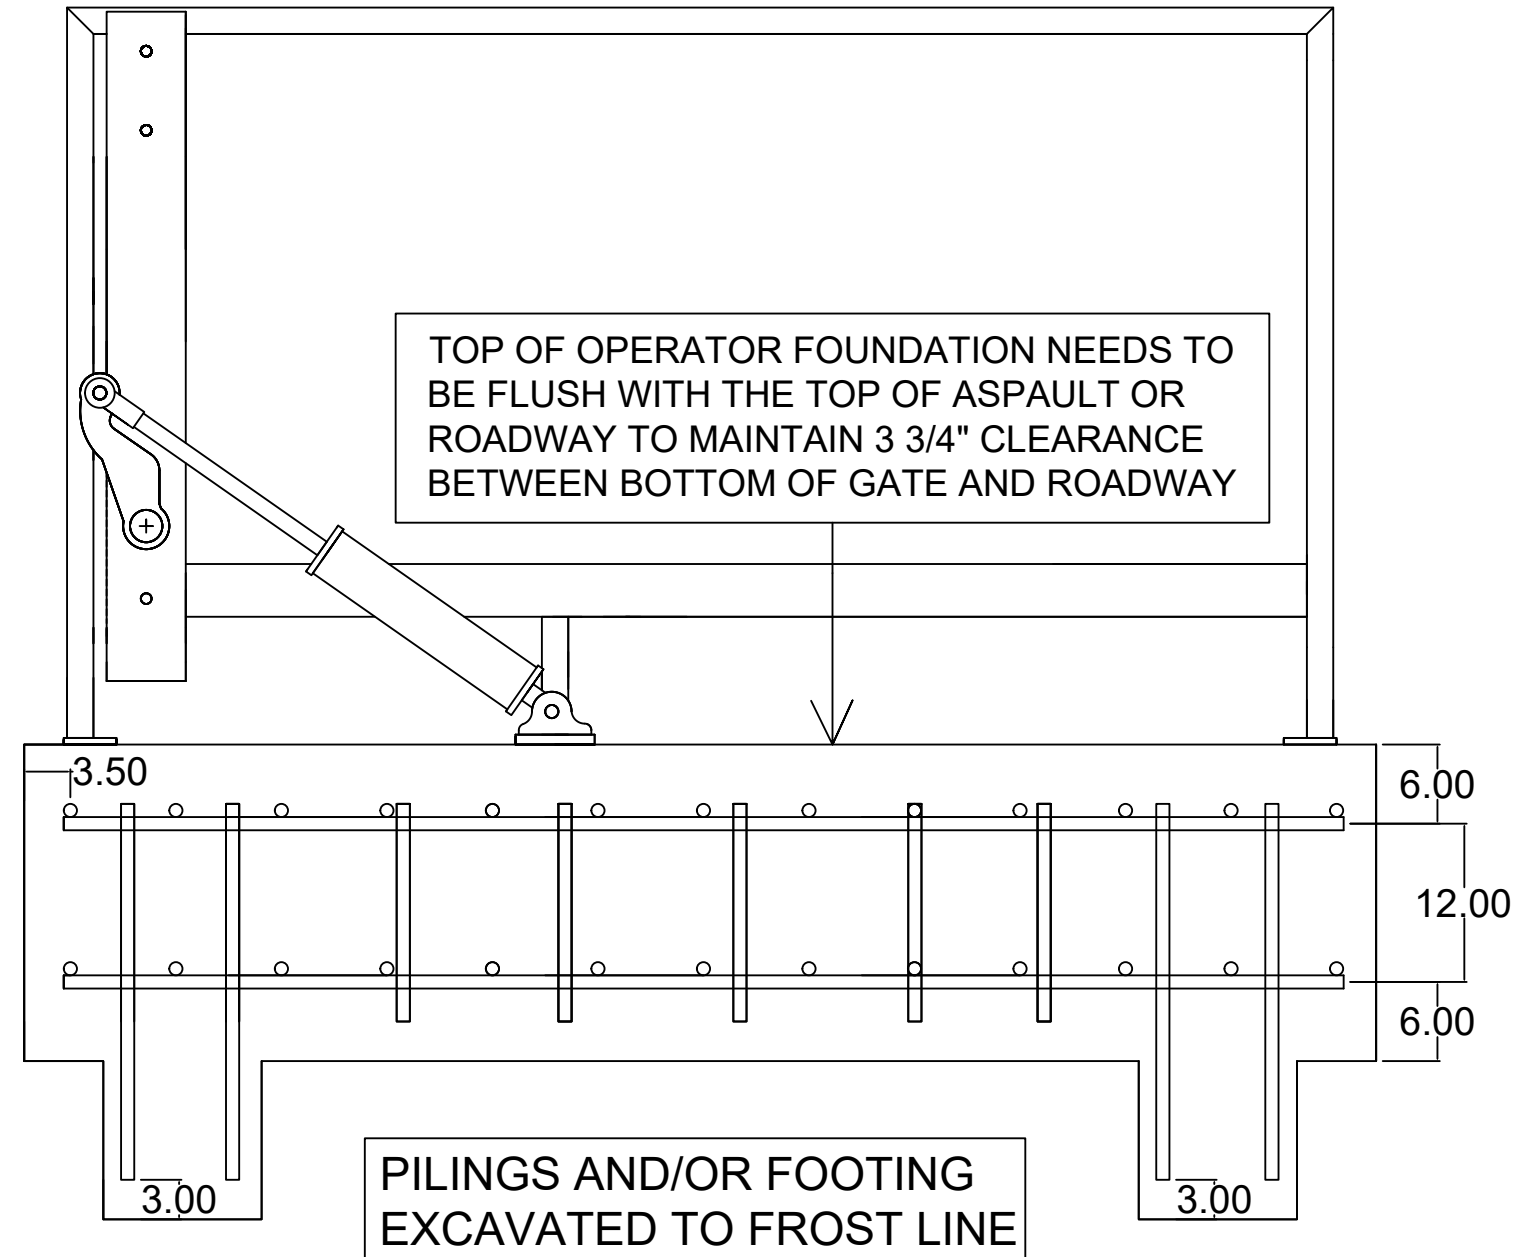


8' Hydraulic Right Hand Operator

Secure Gate Operator to Concrete foundation using quantity 6 - Hilti KWIK BOLT TZ 304 Stainless wedge anchors (5/8" Diameter x 8.5" long)
- Minimum effective embed depth = 4"

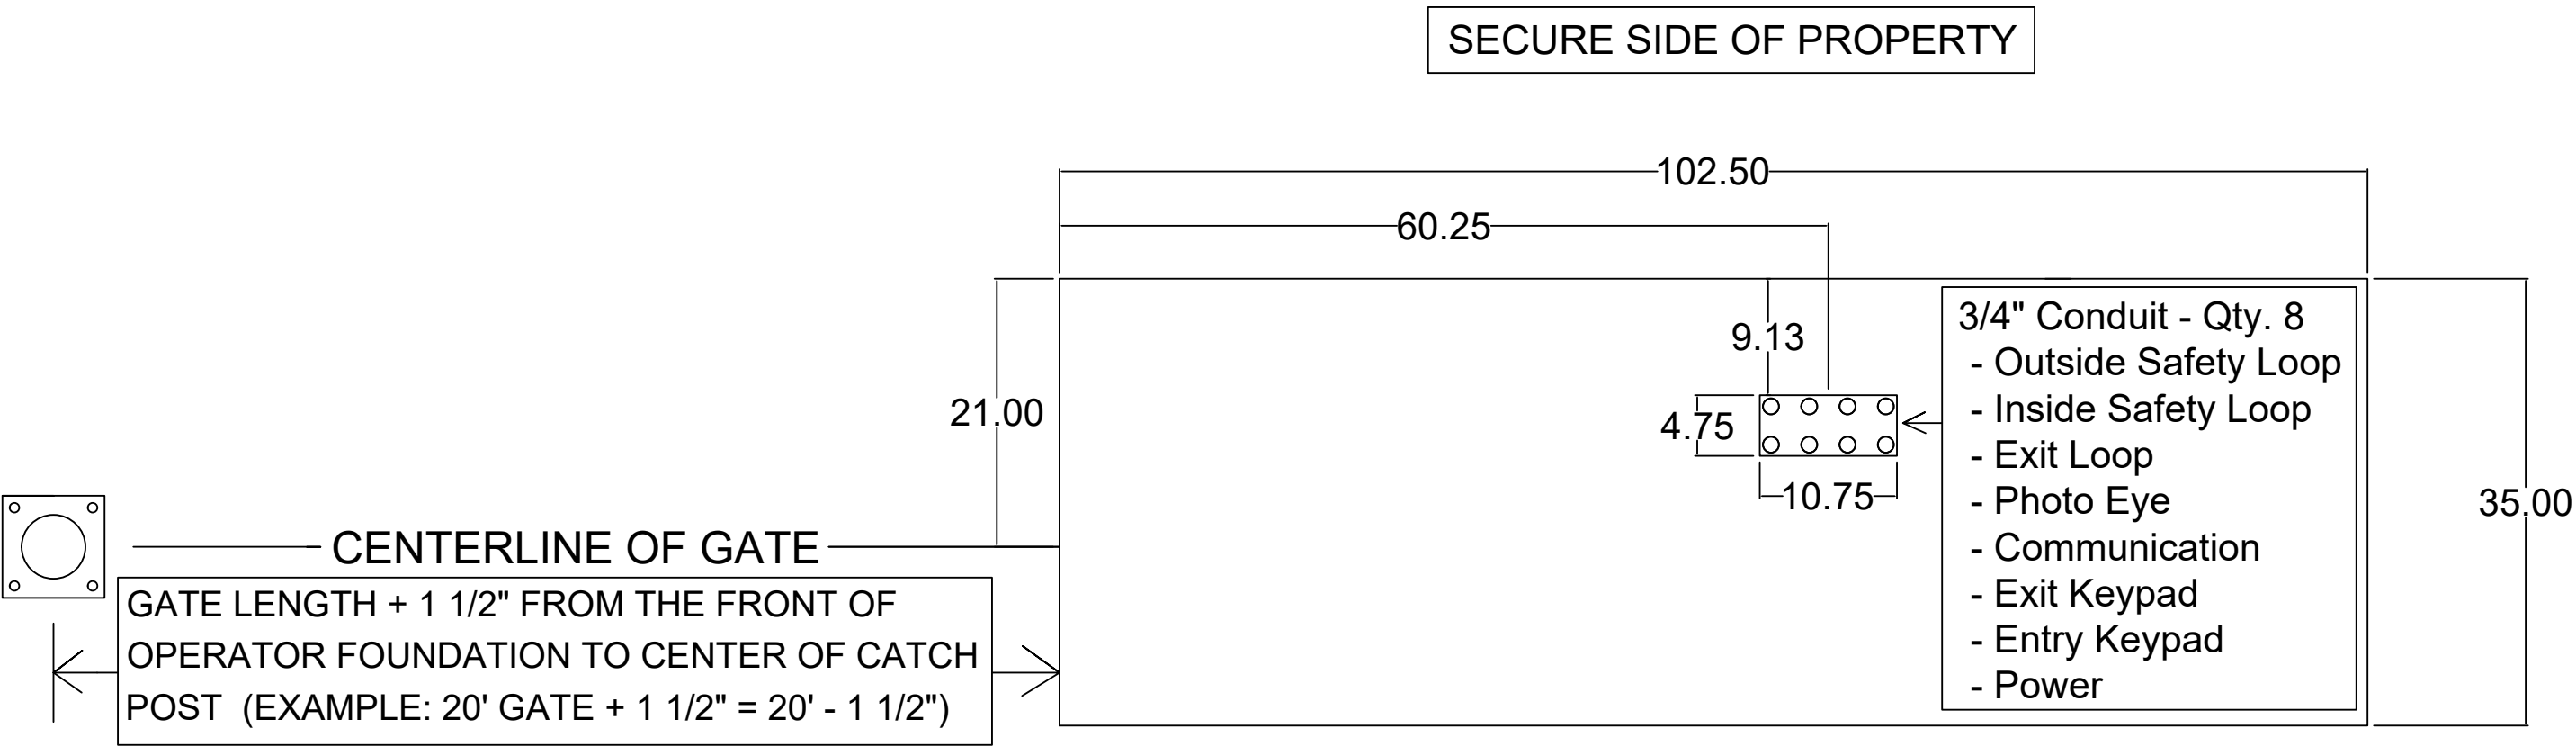

8' HYDRAULIC RIGHT HAND OPERATOR

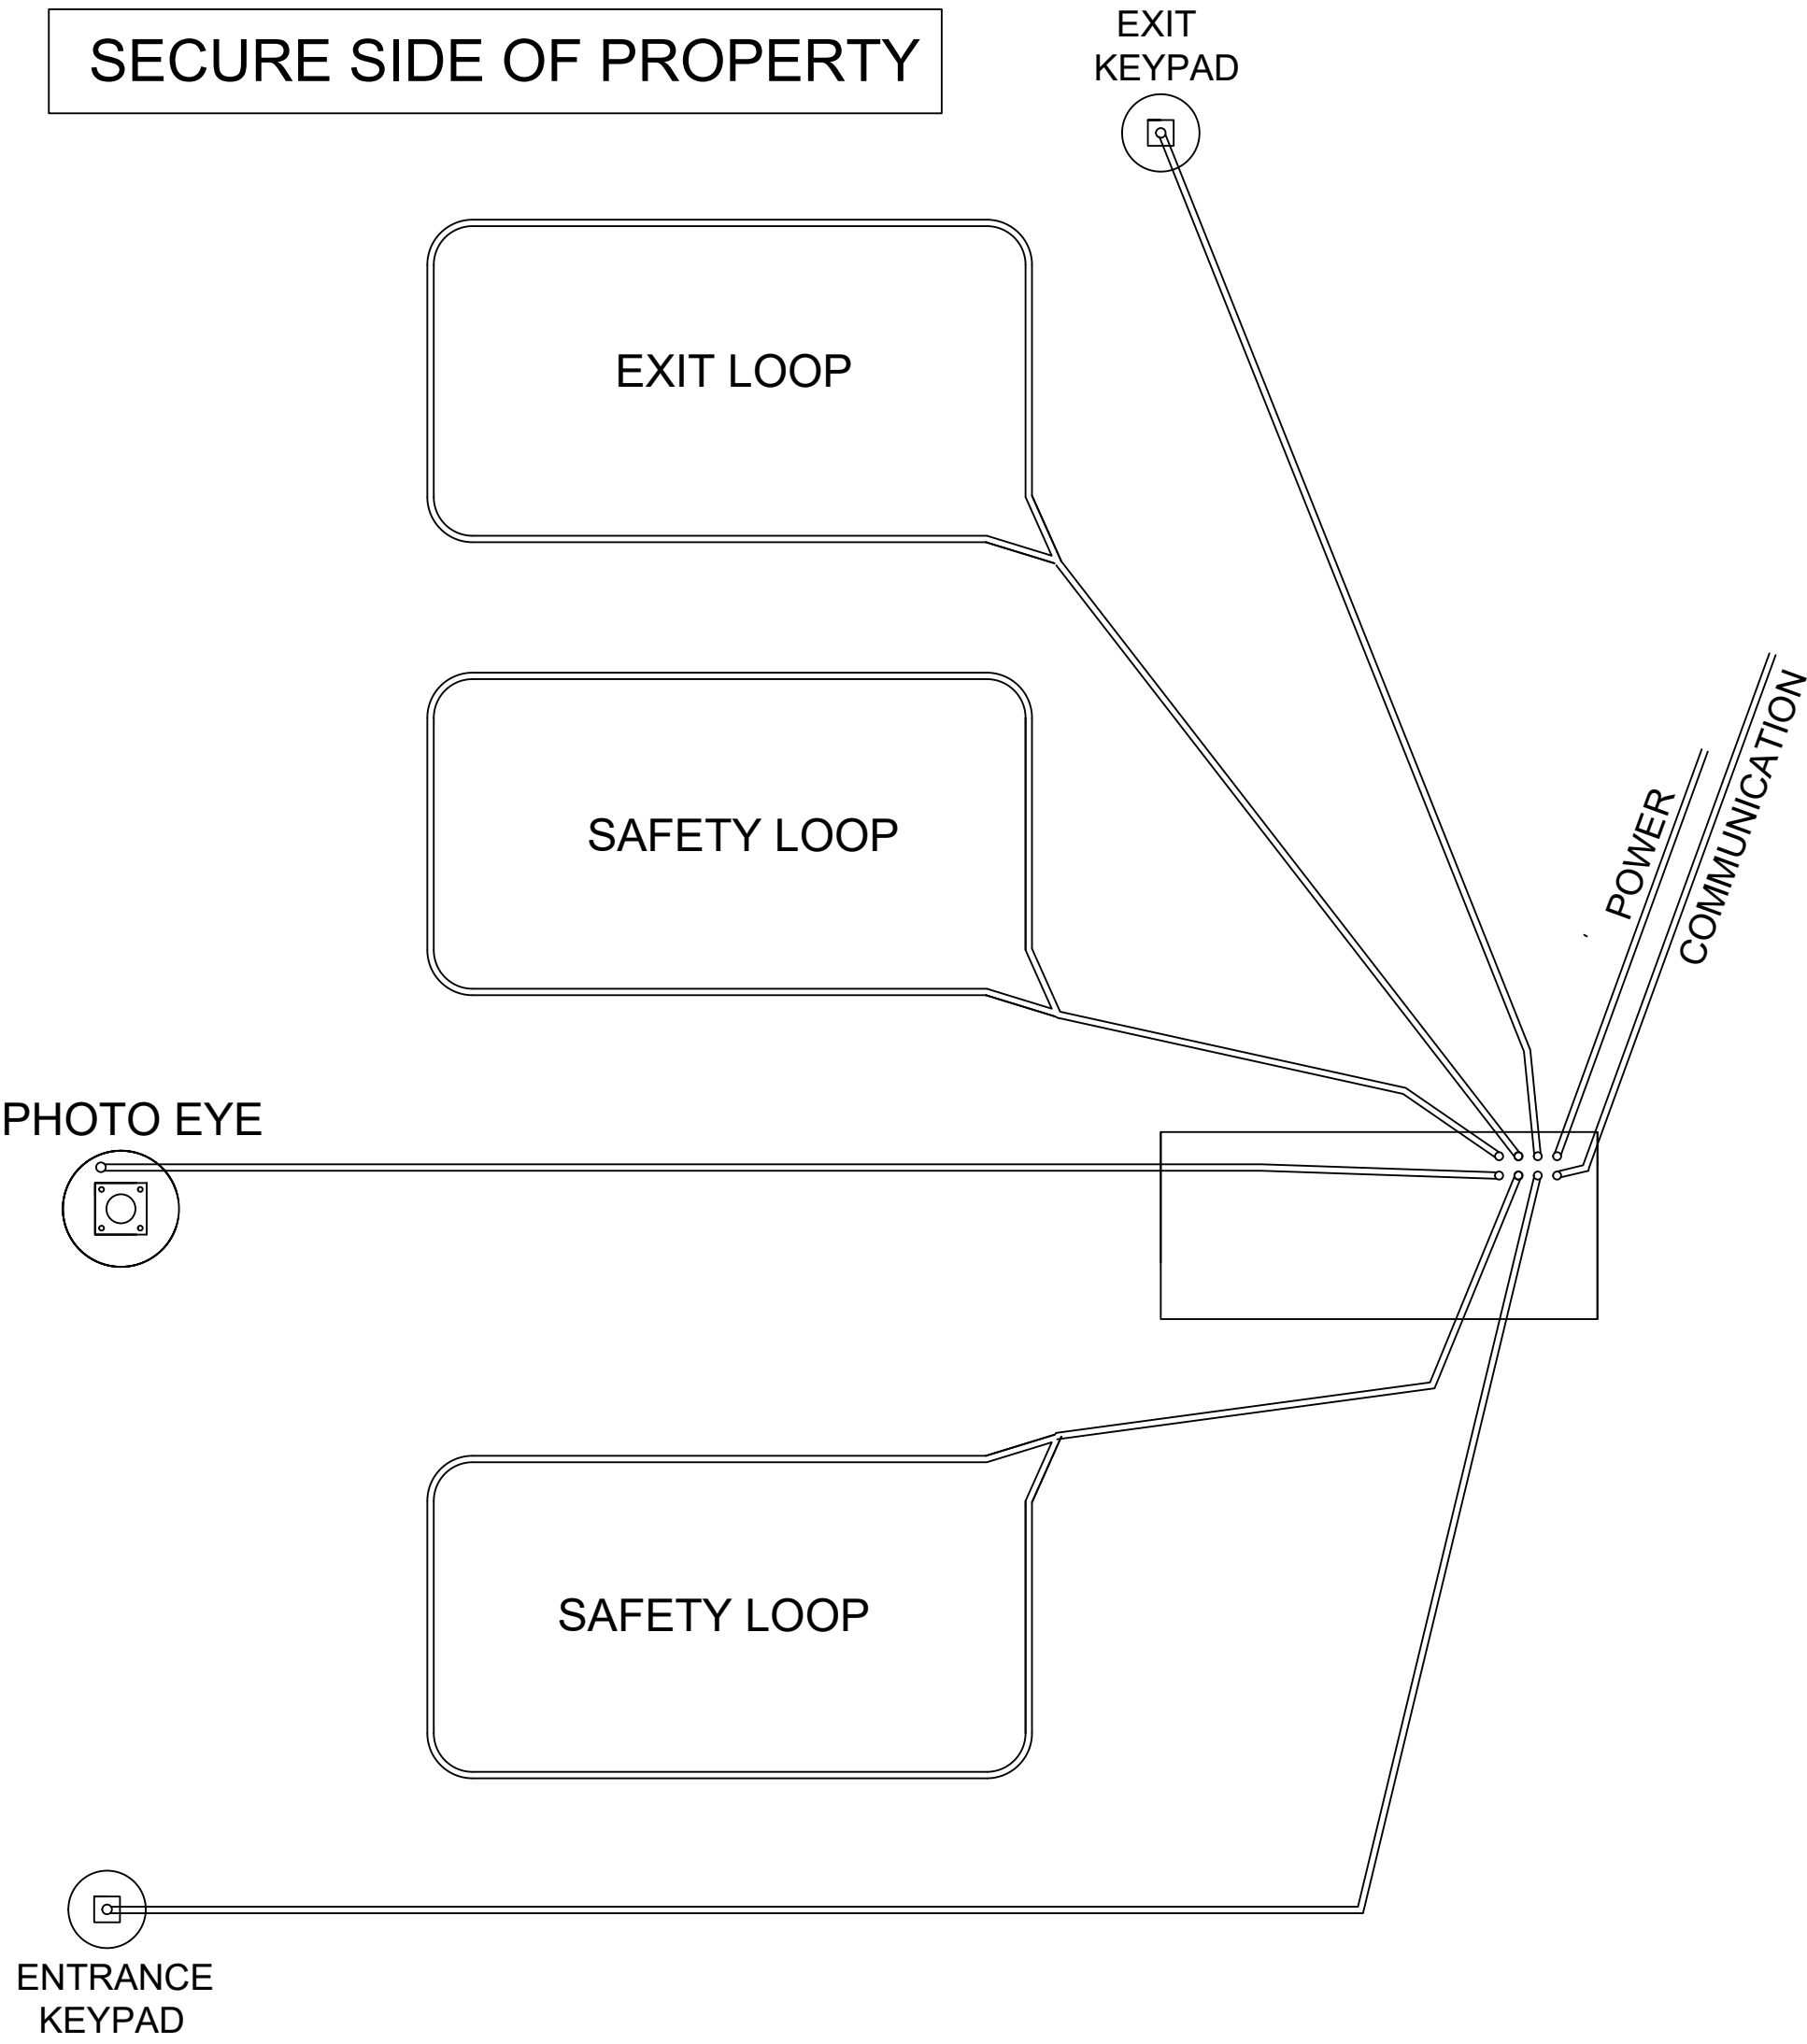

CONDUIT LAYOUT SHOWN FOR RIGHT HAND OPERATOR
*DRAWING IS FOR REFERENCE ONLY

